

OWNER:

CONTRACTOR:

PROJECT NAME :

ARCHITECTURE :

STRUCTURE ENGINEERS :

MACHANICAL ENGINEERS :

ENVIRONMENT ENGINEERS :

SANITARY ENGINEERS :

ELECTRICAL ENGINEERS :

DRAWING TITLE :

ROOF PLAN

SCALE A1

Date

REVISION


DATE


CHECKED :

APPROVED :


DWG.NUMBER

PAPER SIZE : A1

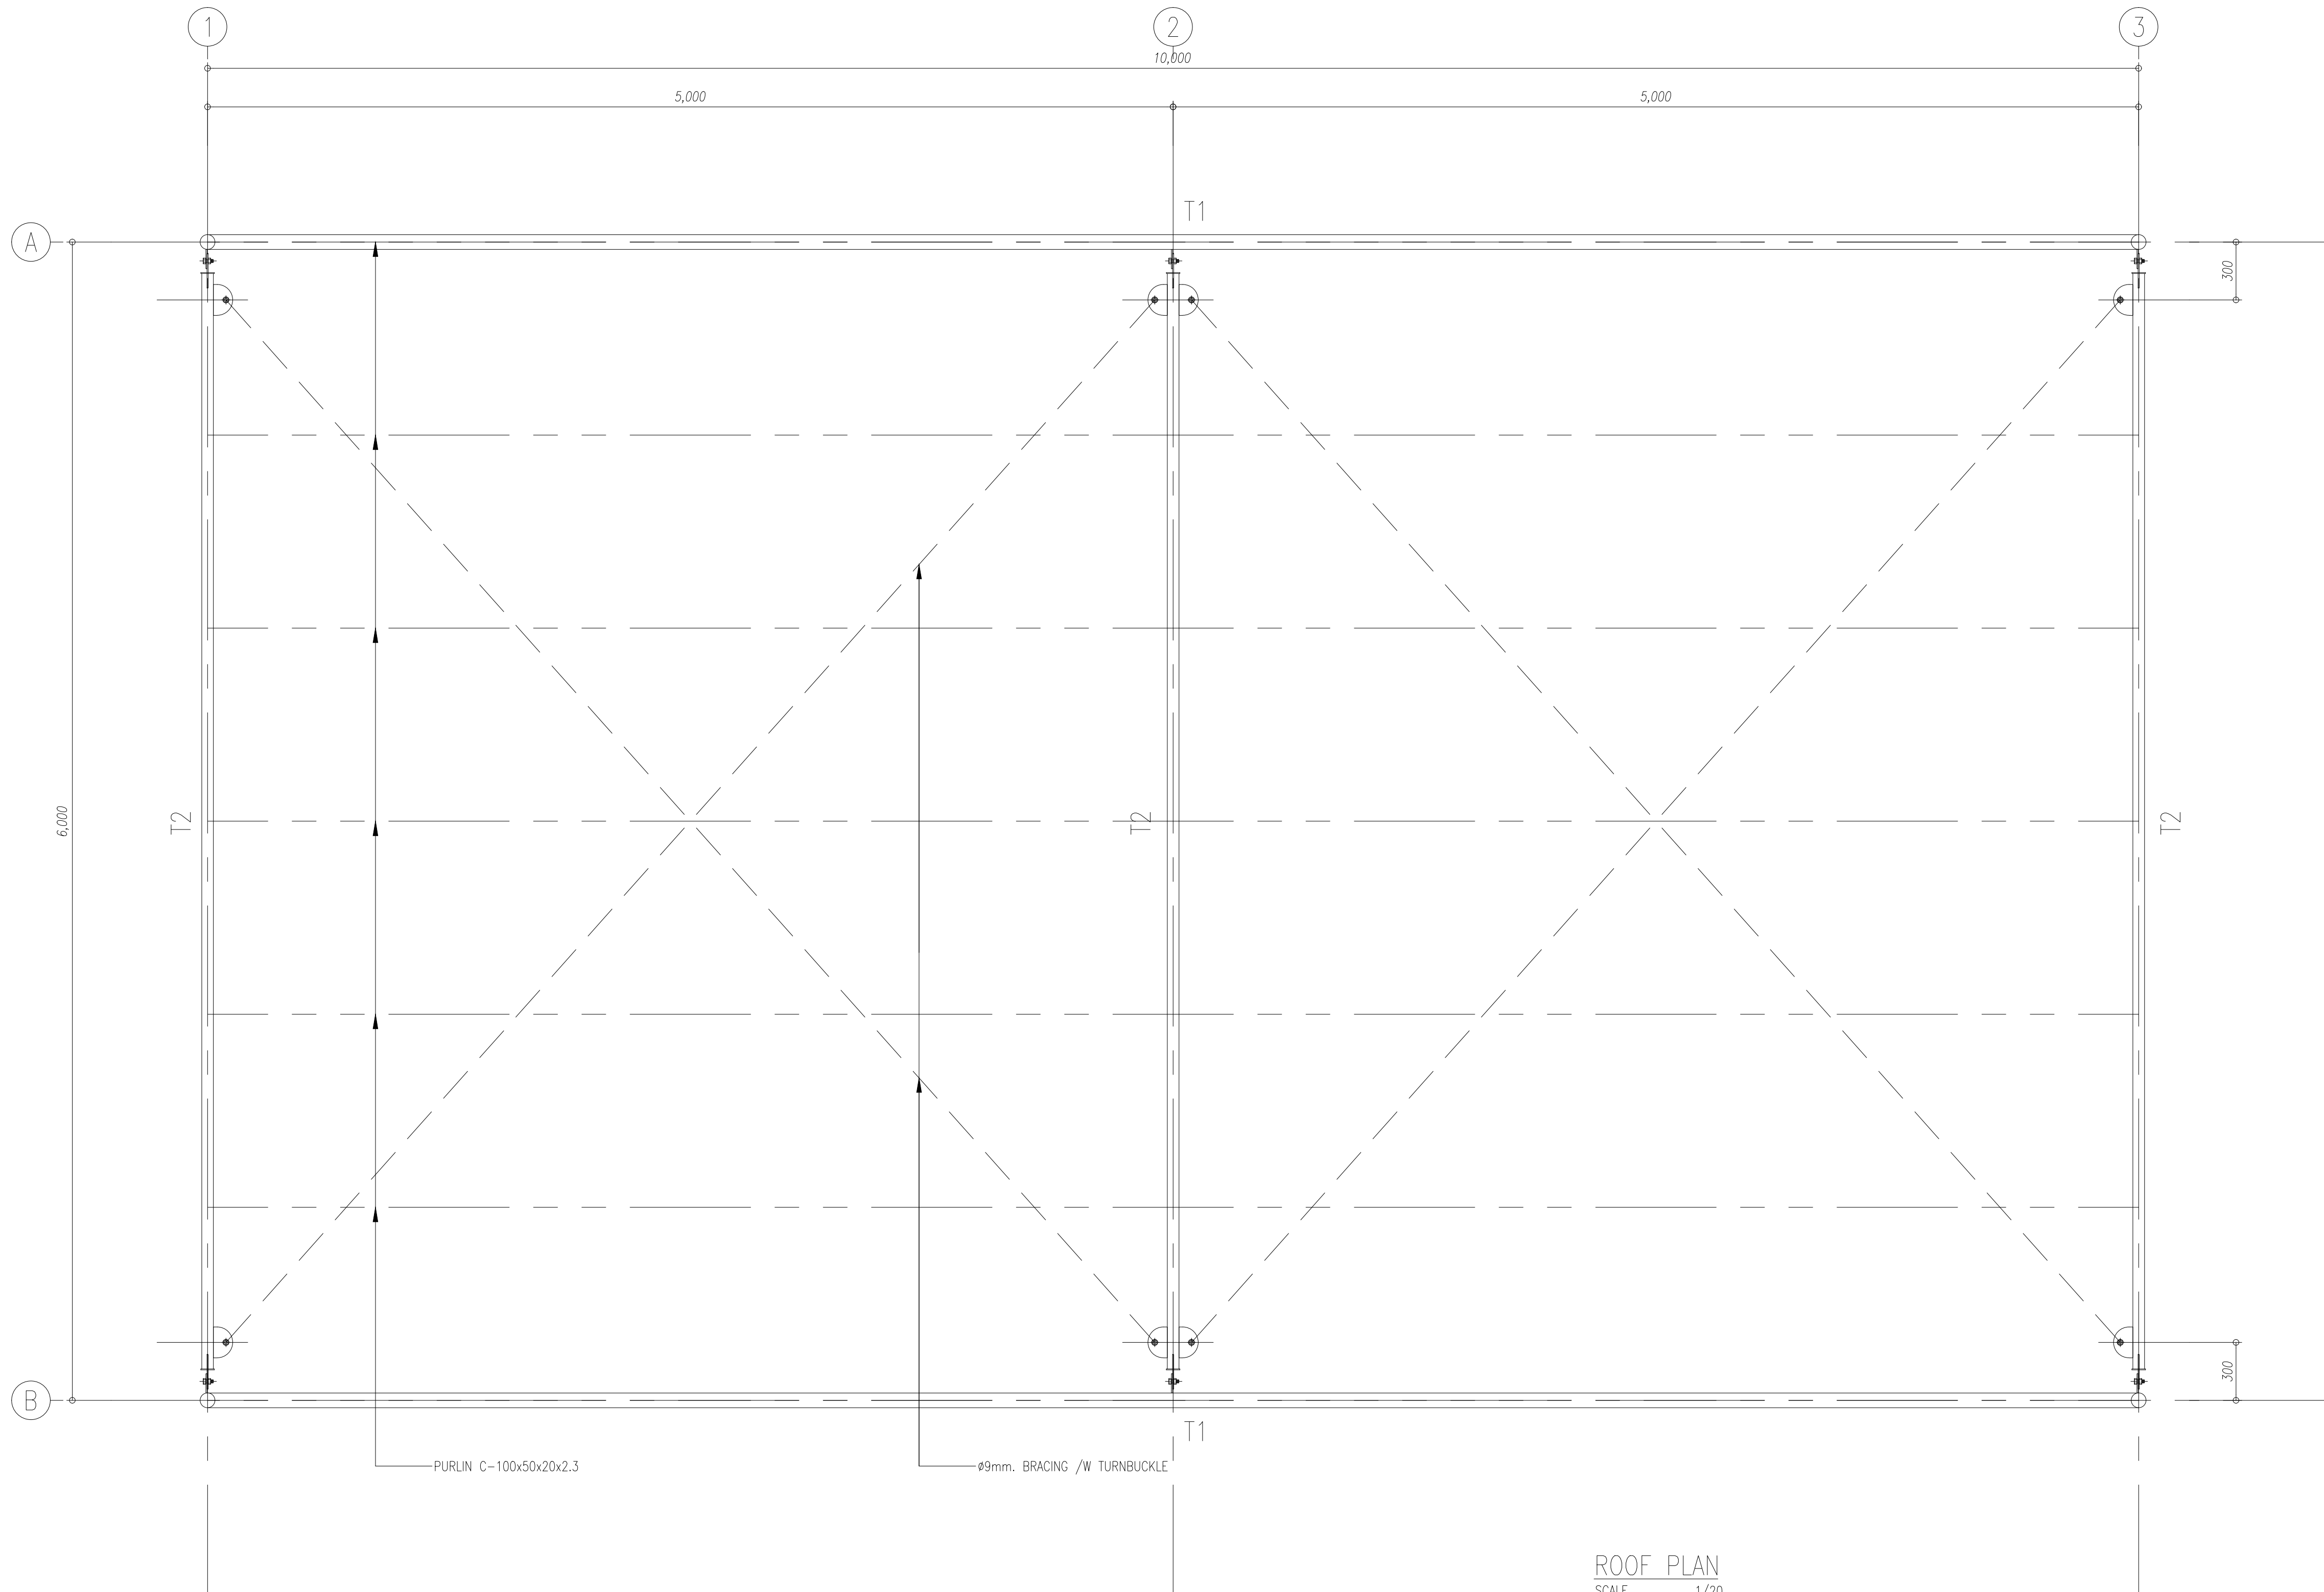

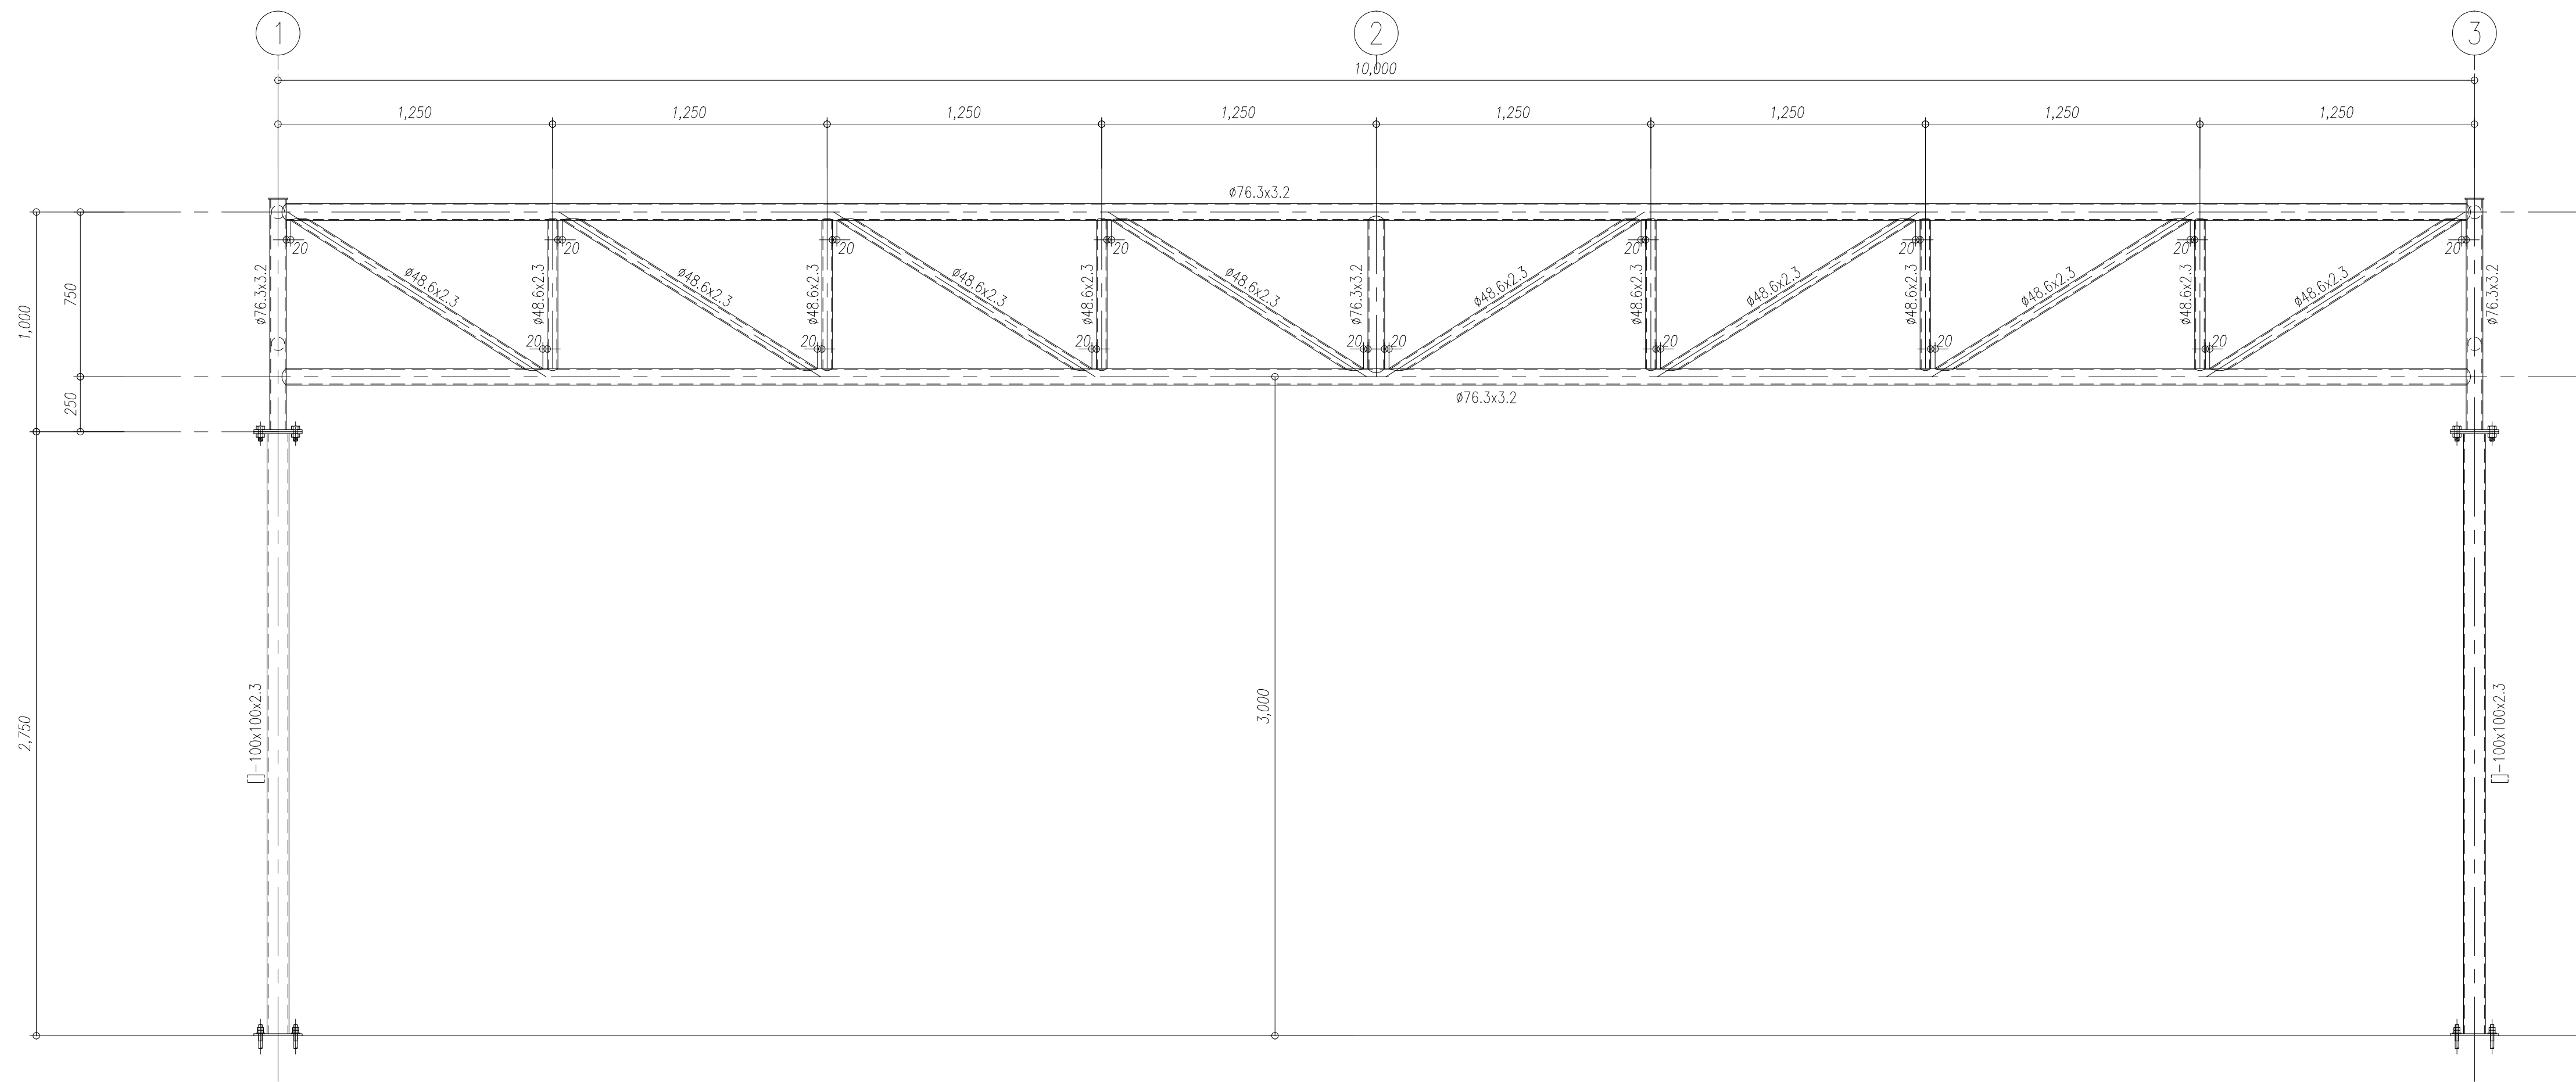

FRAMING ELEVATION LINE B
SCALE 1/20

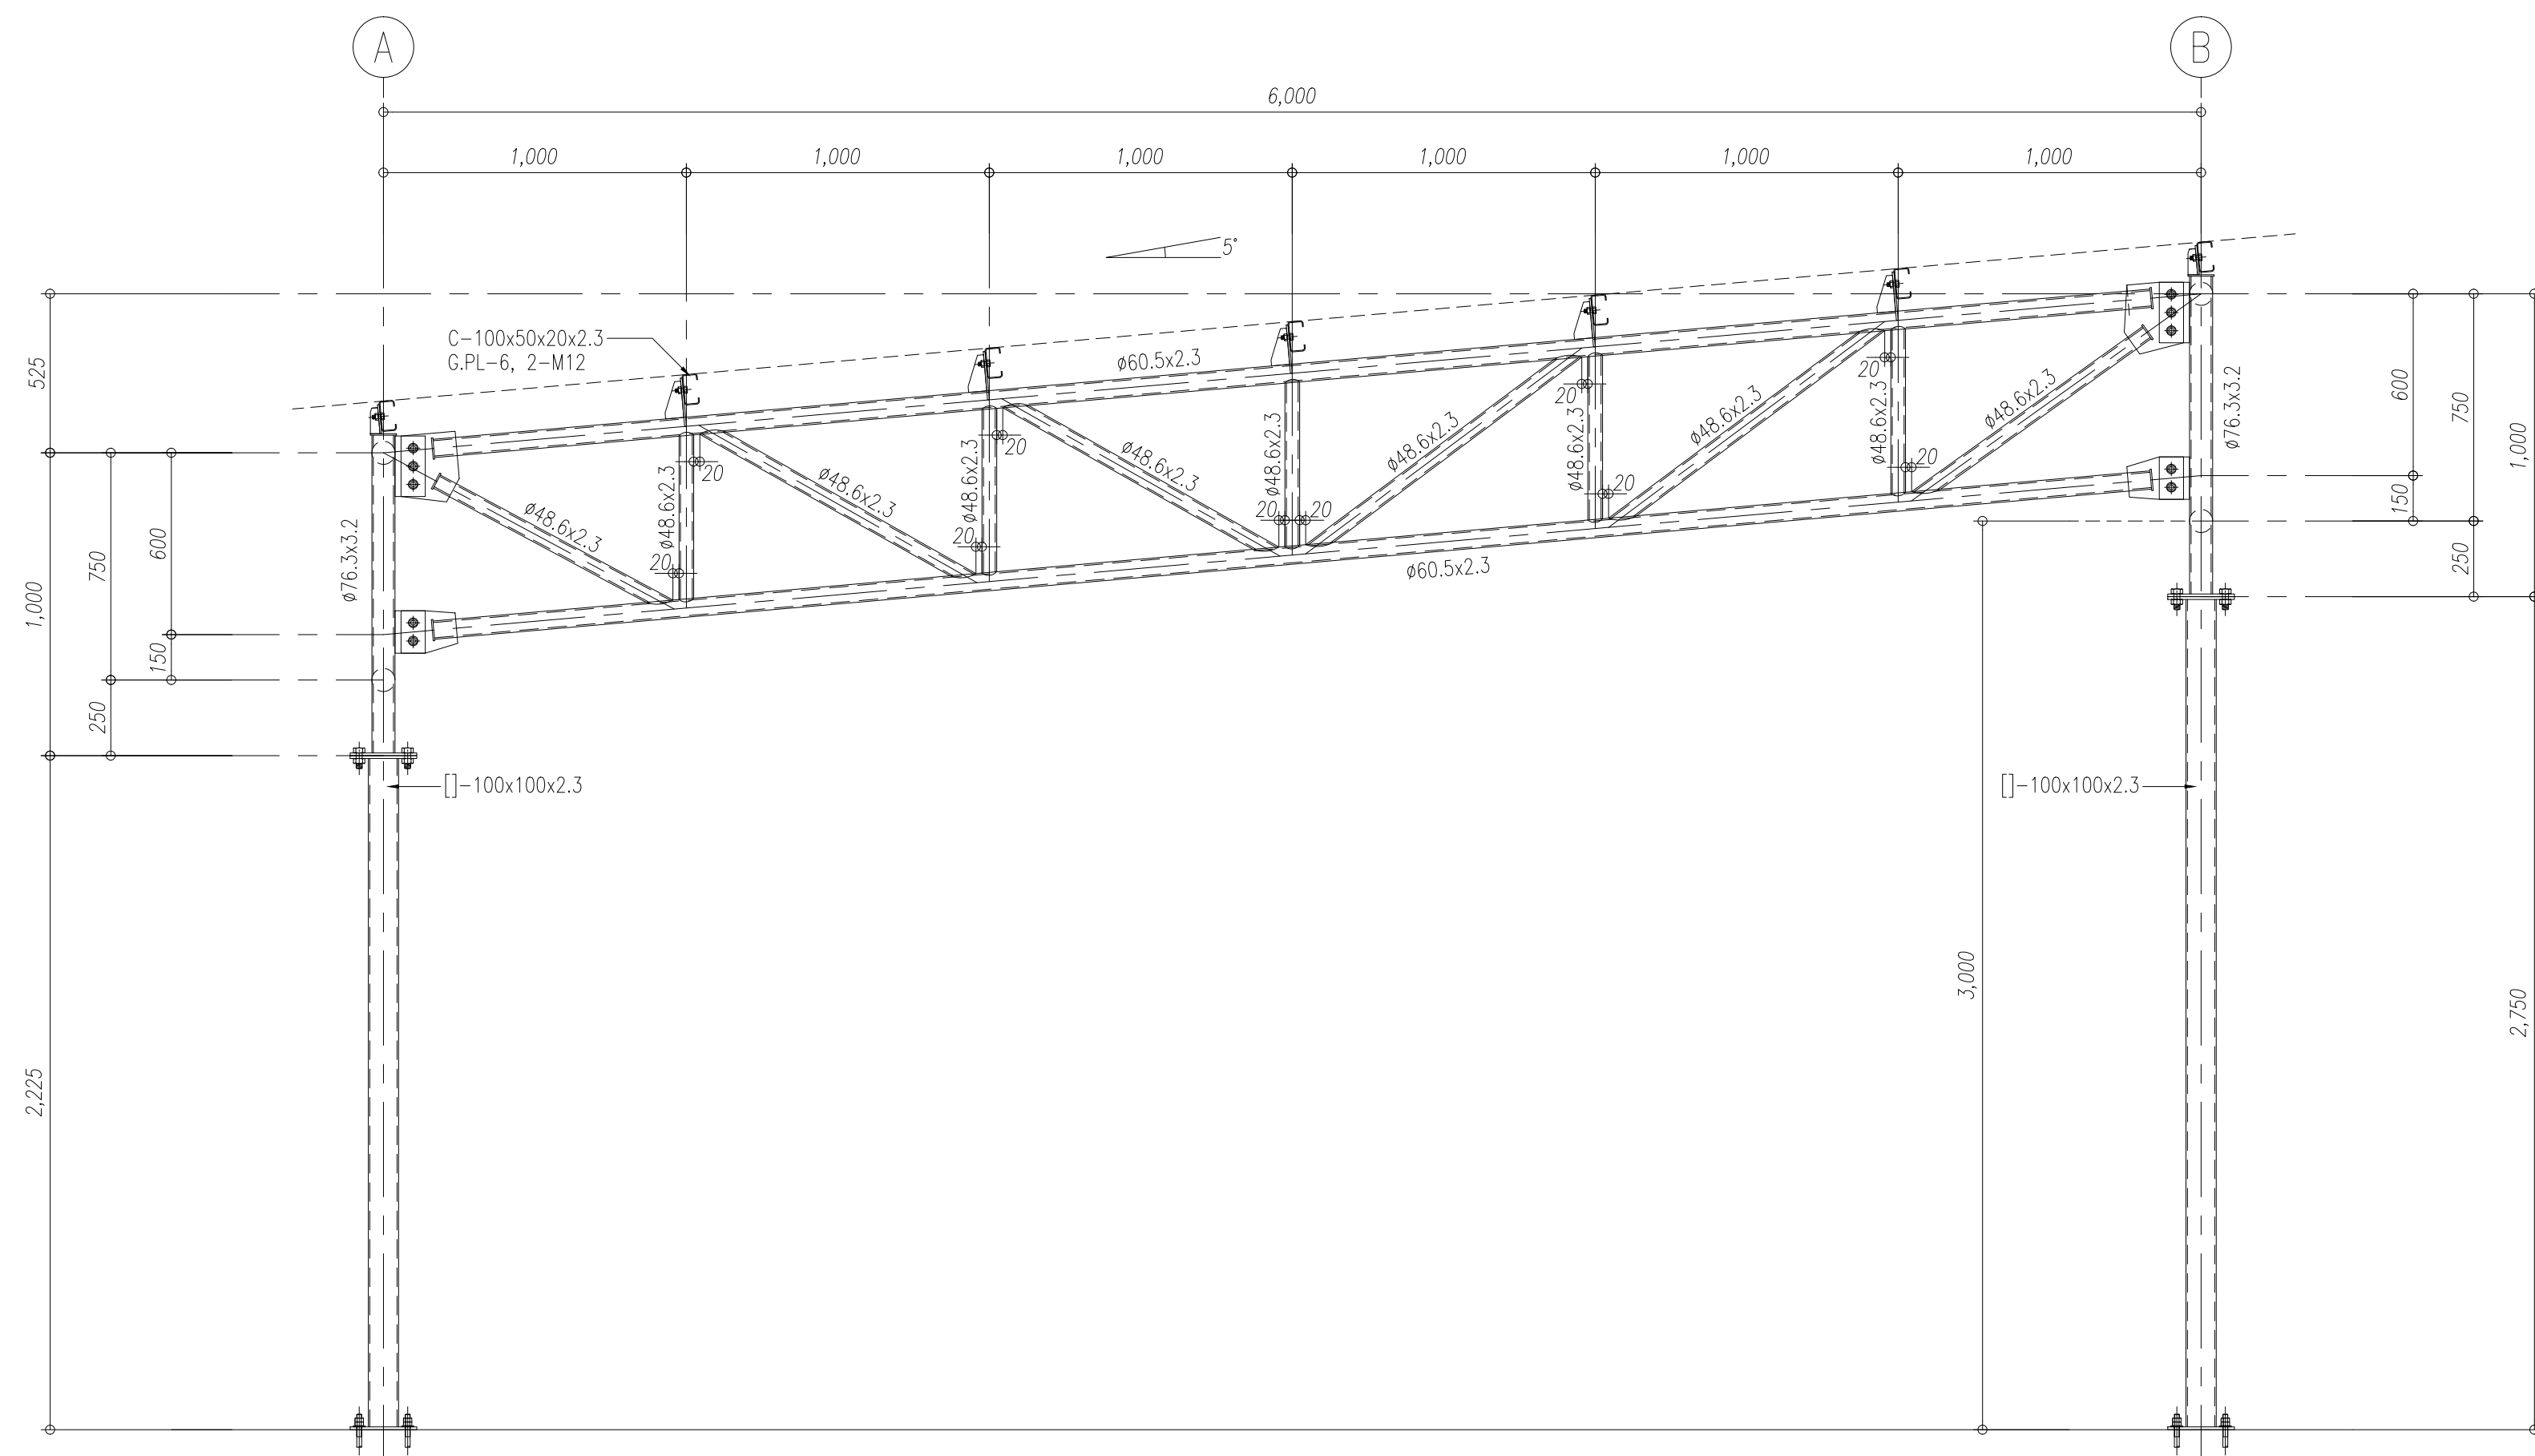

FRAMING ELEVATION LINE 1
SCALE 1/20

OWNER:

CONTRACTOR:

PROJECT NAME :

ARCHITECTURE :

STRUCTURE ENGINEERS :

MACHANICAL ENGINEERS :

ENVIRONMENT ENGINEERS :

SANITARY ENGINEERS :

ELECTRICAL ENGINEERS :

DRAWING TITLE :

FRAMING ELEVATION

SCALE A1

Date

REVISION



DATE

CHECKED :

APPROVED :

DWG.NUMBER

PAPER SIZE : A1

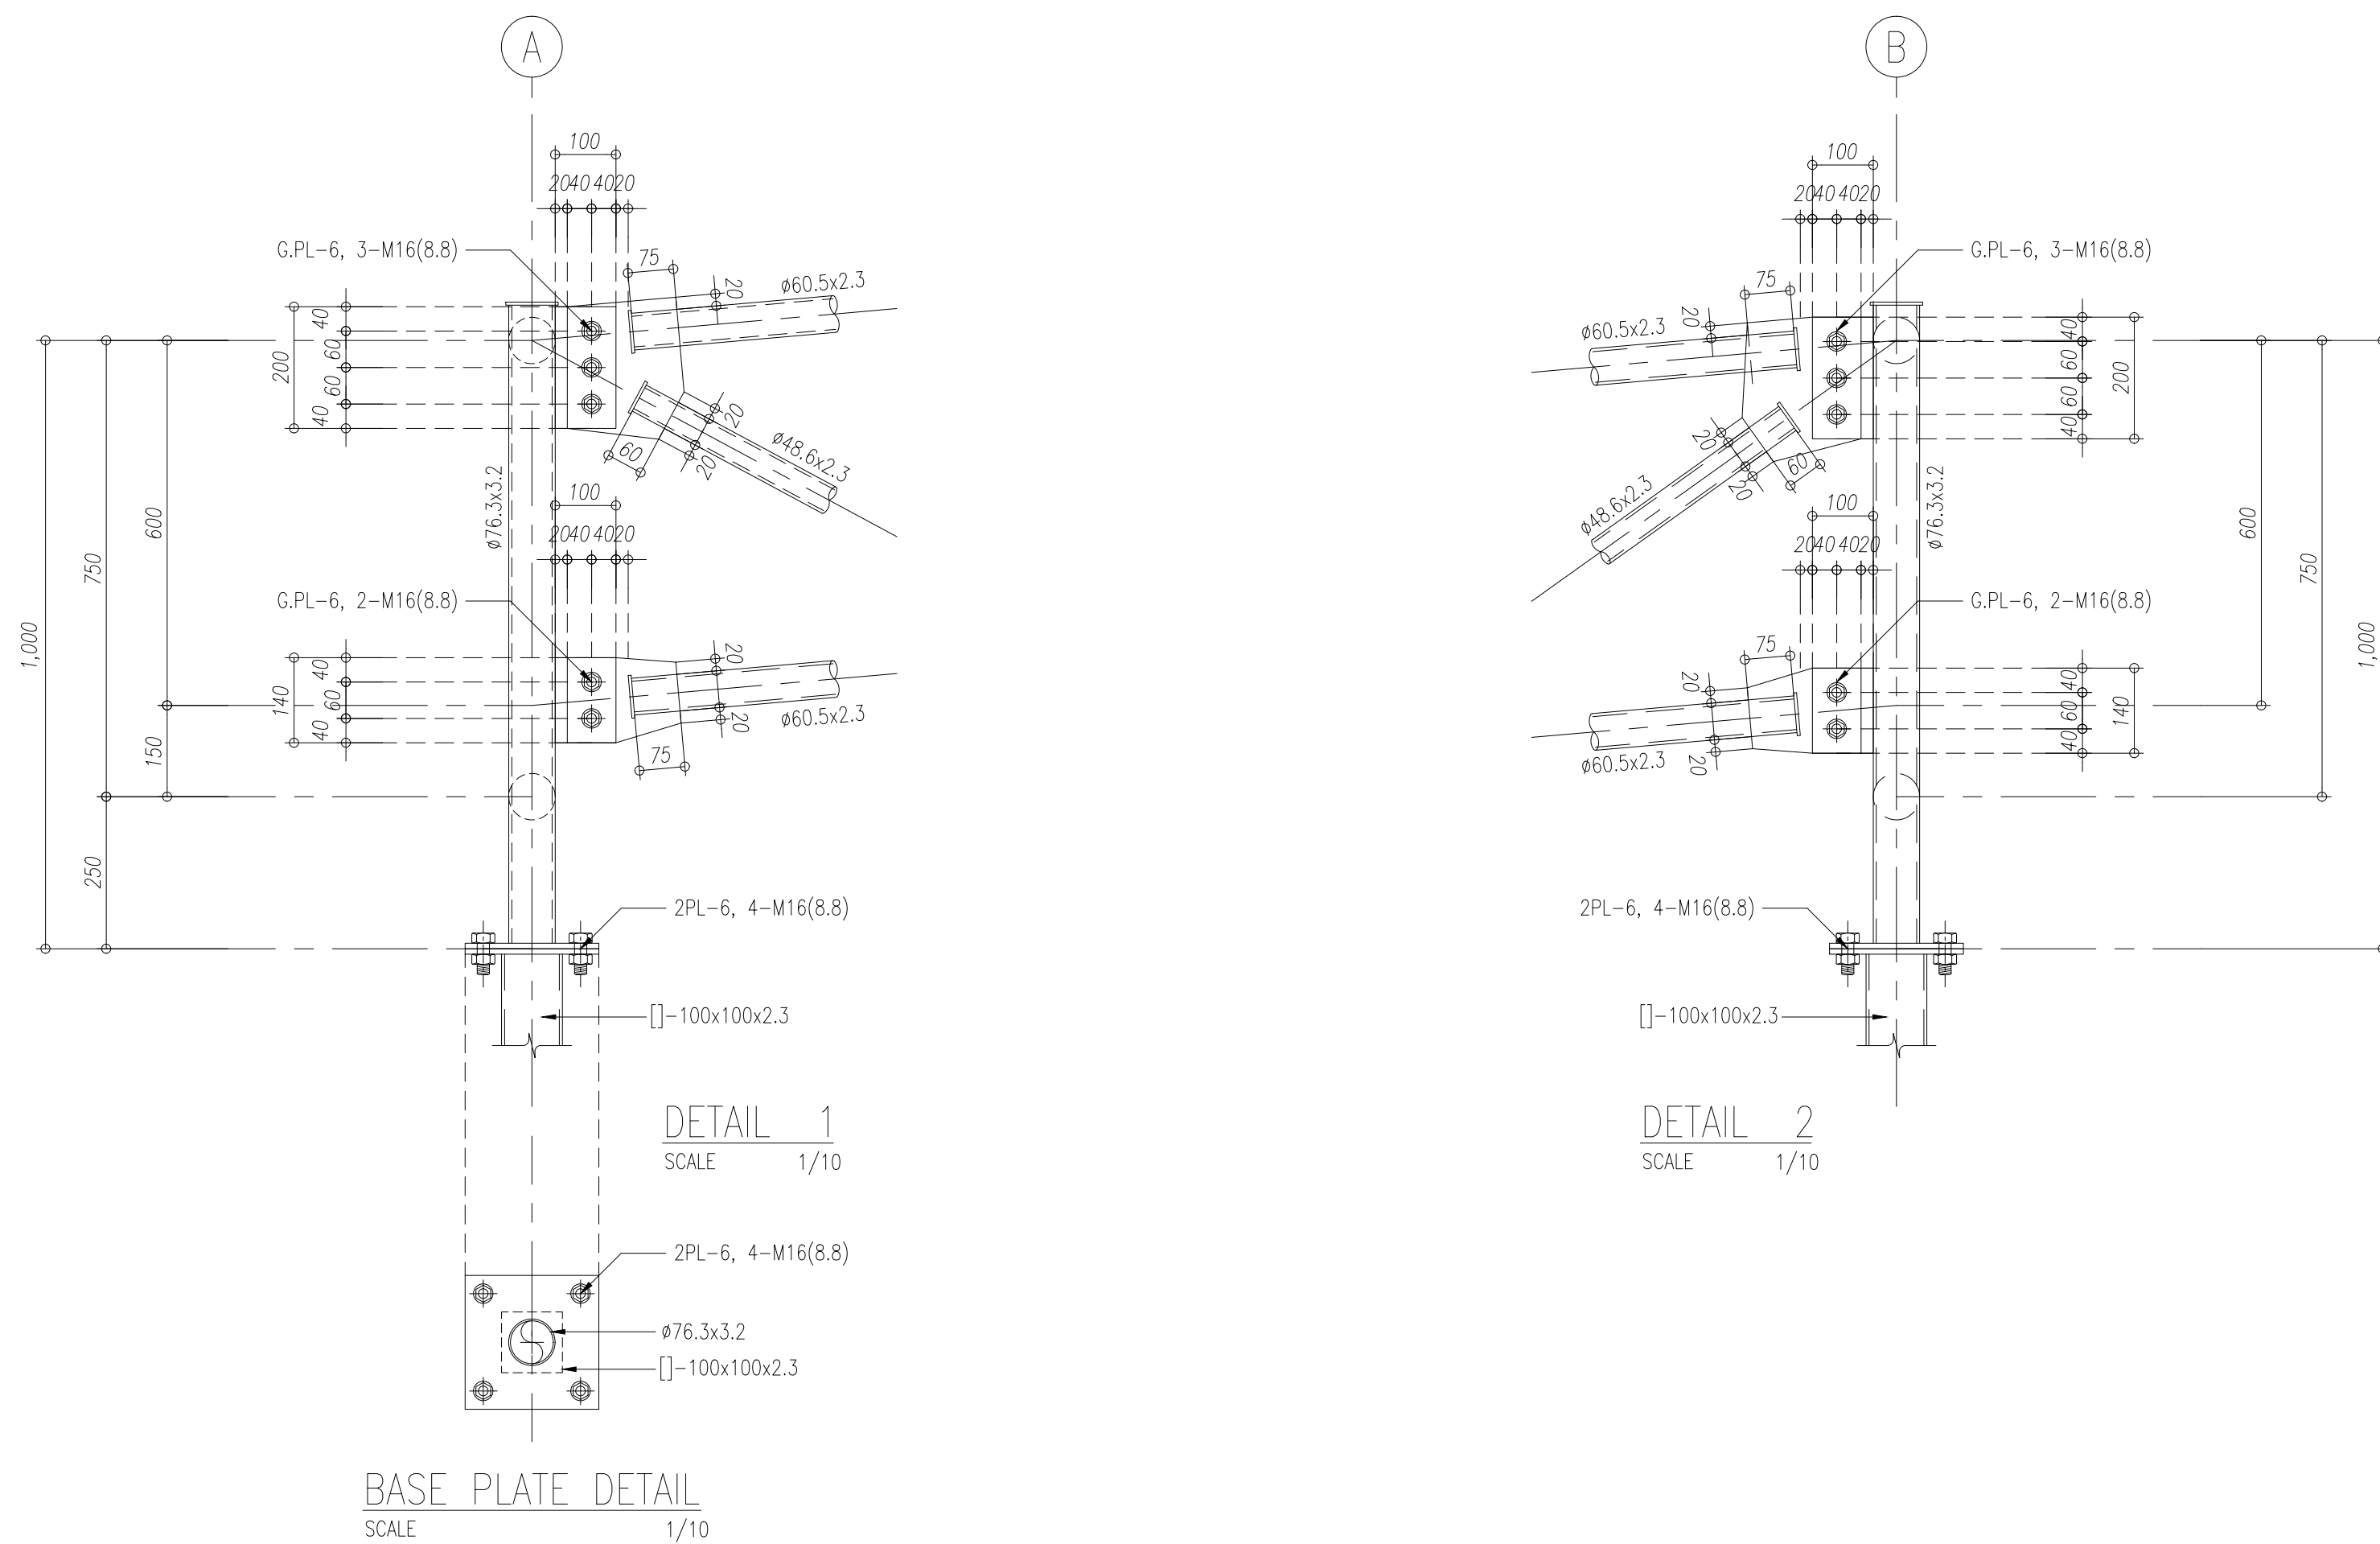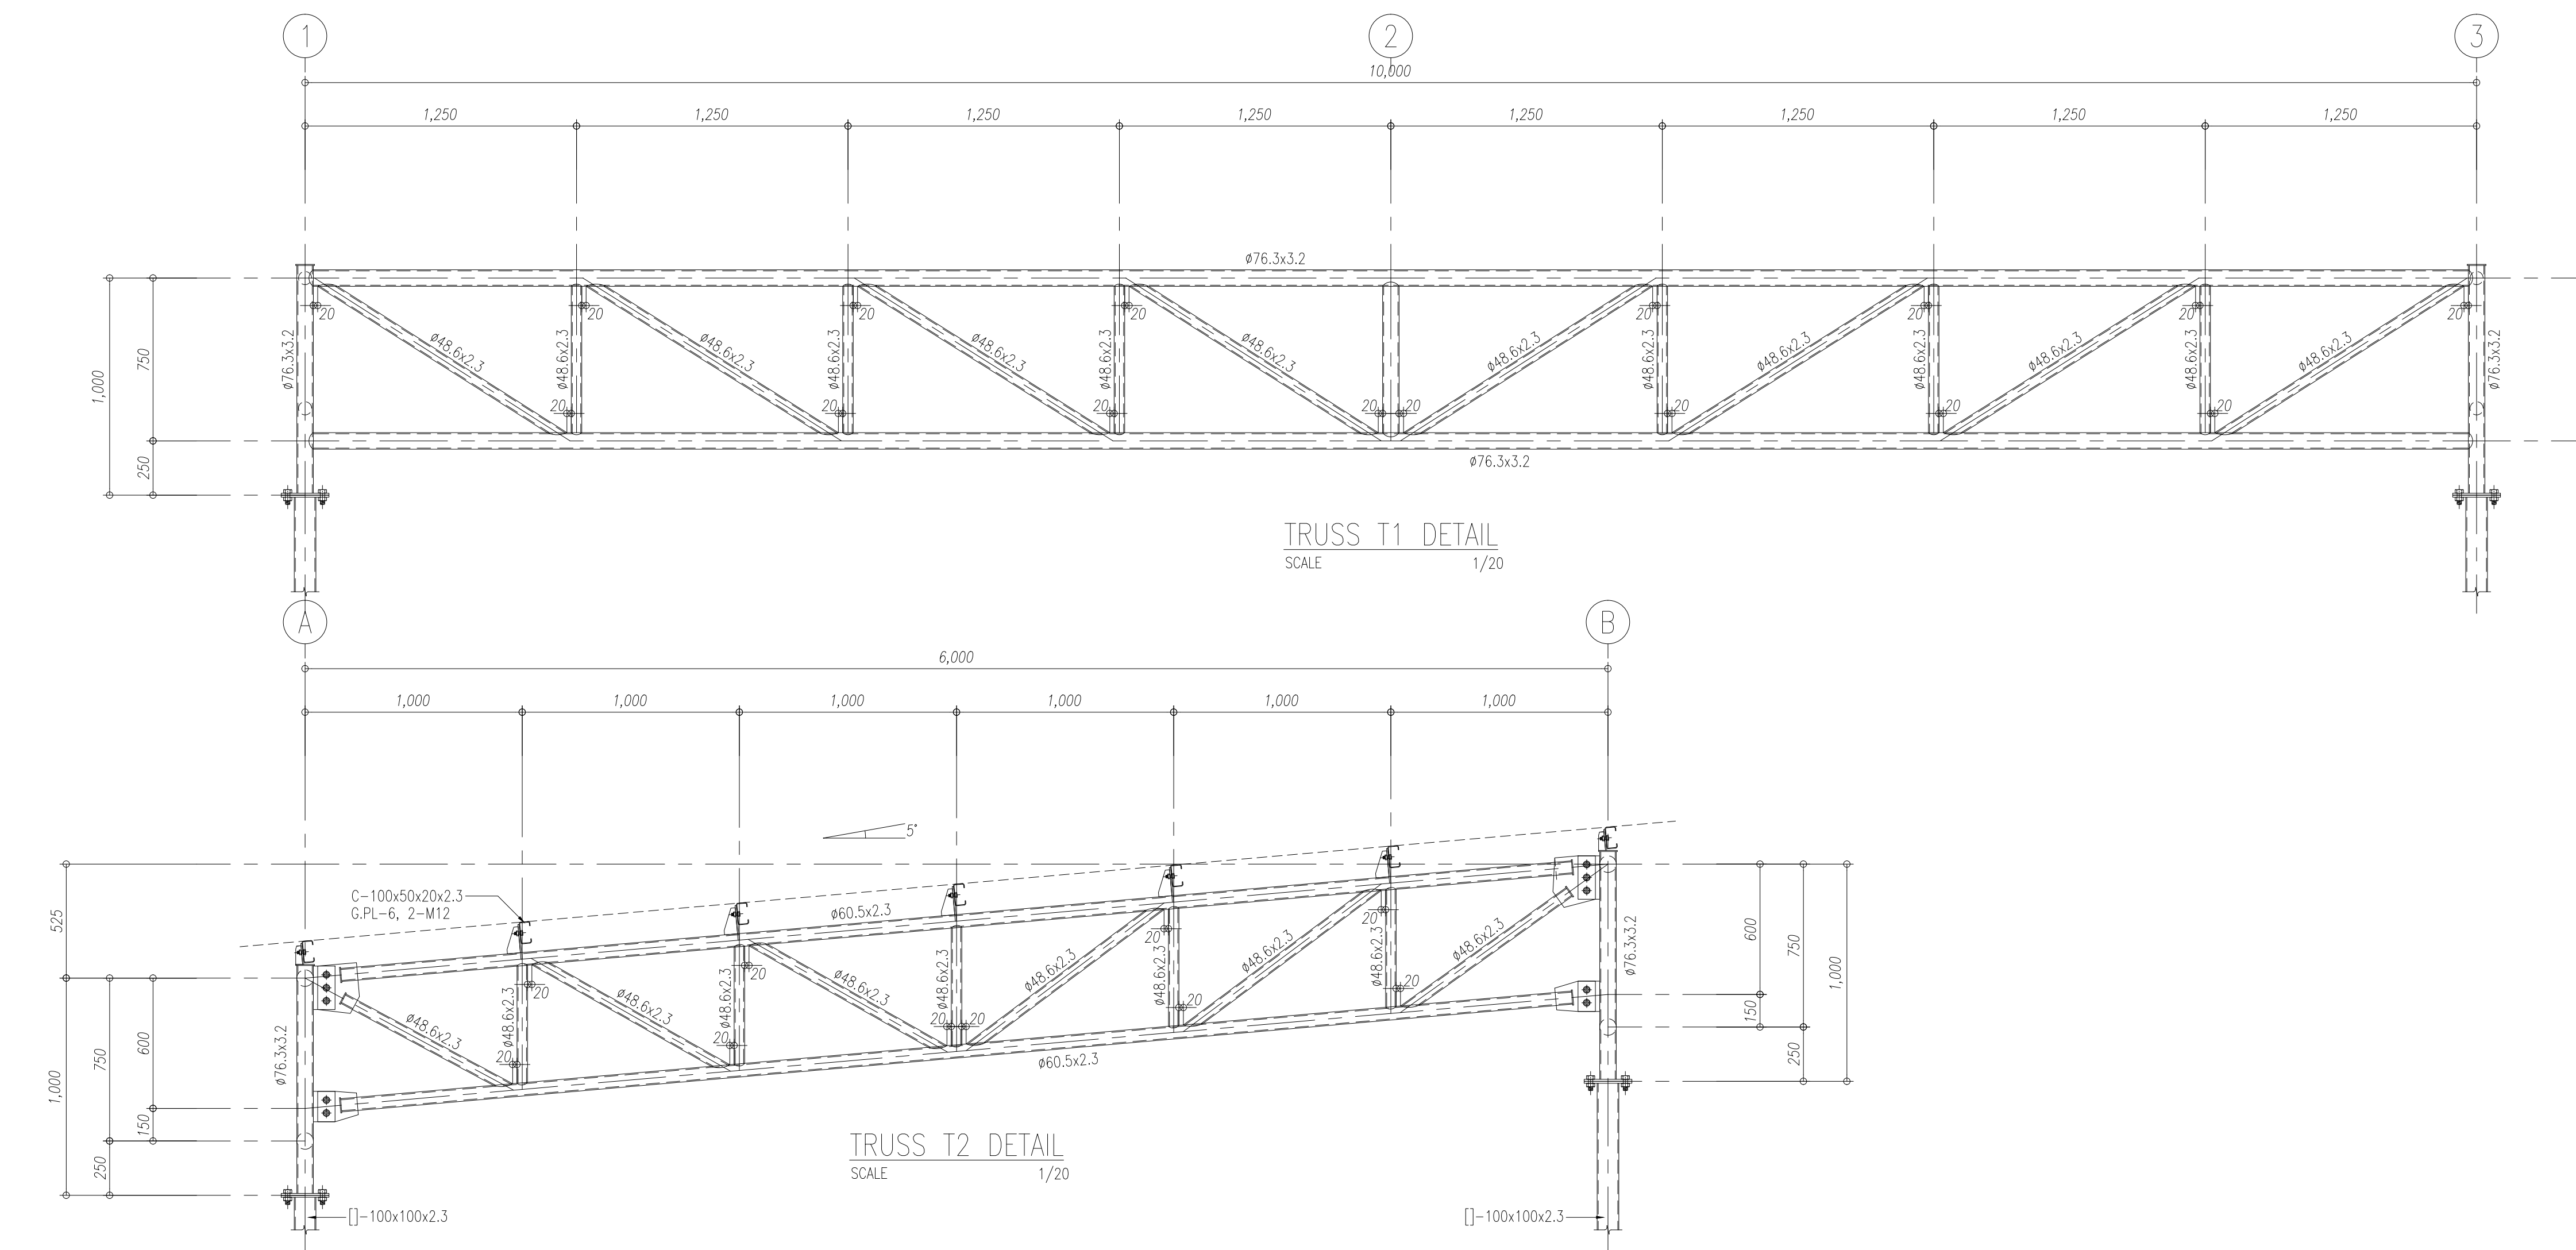

OWNER:

CONTRACTOR:

PROJECT NAME :

ARCHITECTURE :

STRUCTURE ENGINEERS :

MECHANICAL ENGINEERS :

ENVIRONMENT ENGINEERS :

SANITARY ENGINEERS :

ELECTRICAL ENGINEERS :

DRAWING TITLE :

TRUSS DETAIL

SCALE A1

Date

REVISION

DATE

CHECKED :

APPROVED :

DWG.NUMBER

PAPER SIZE : A1